番号	部品名	枠区分	員数	基本寸法	切断寸法
1	中間扉ストッパー	四方枠	4	−	−
2	トラス小ネジM4×4	四方枠	4	−	−
3	ロットNo.ラベル	四方枠	1	−	−
4	両面テープ	四方枠	3	−	200

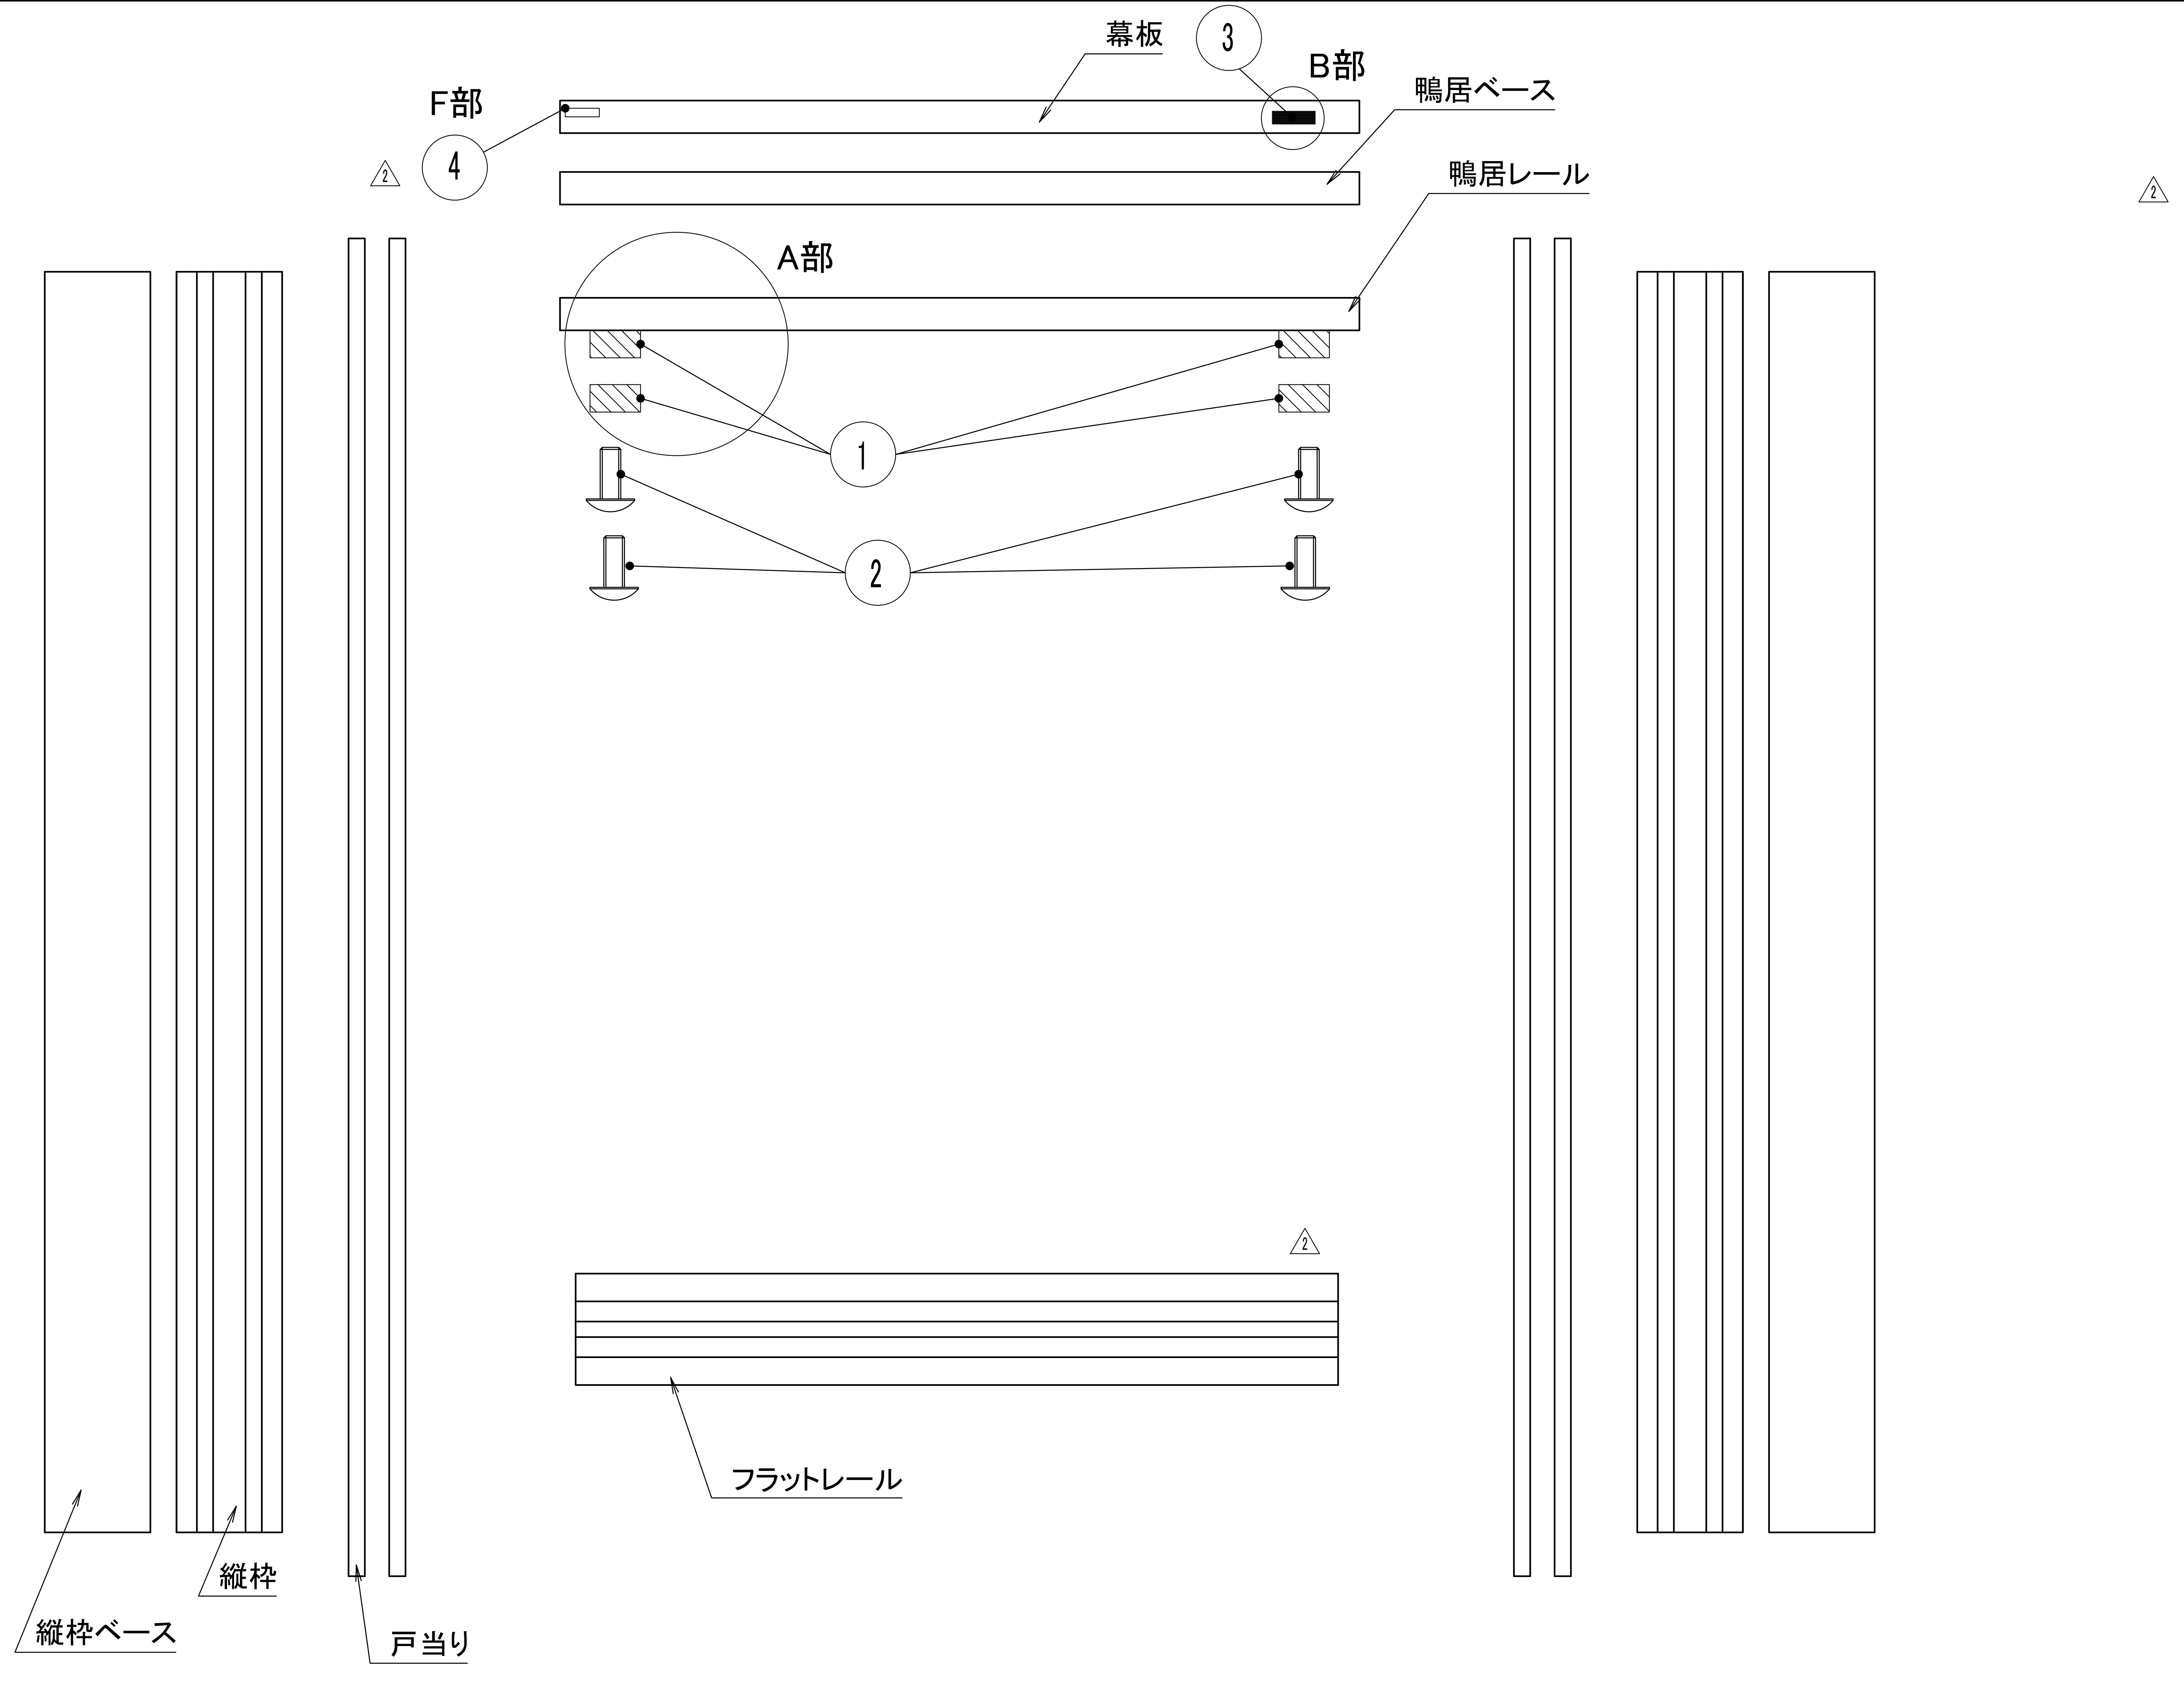

注）1. 形材番号の枝番は最終枝番を使用の事。

2. 各部詳細についてはF466U10004,5を参照の事。

番号	名　称	員数	材質・規格	部品図番	備　考

改訂	記号	年月日	担当	変更理由
	2 −3	21/01/08	李暁楠	設指 TJ-1976 ラベル削除
	1 −1	14/09/12	車文華	設指 TH-9137 機種追加
	△	13/05/10	李暁楠	設指 TH-8499 機種追加

仕上		熱処		表処		公差	

尺度		日付	13/05/02	承認	黒石	検図	木内	設計	吉田アキ	製図	李暁楠
角法	三　角　法			名称	F466 大東建託様向けアルミスクリーン枠 引違2枚建て アッセンブリ図						
株式会社 LIXIL				図番	F466U10011						

承認日：2021/01/07